
# [3] Project Architecture

*Sheet hierarchy and signal flow. Click a block or its page number to open the sheet.*

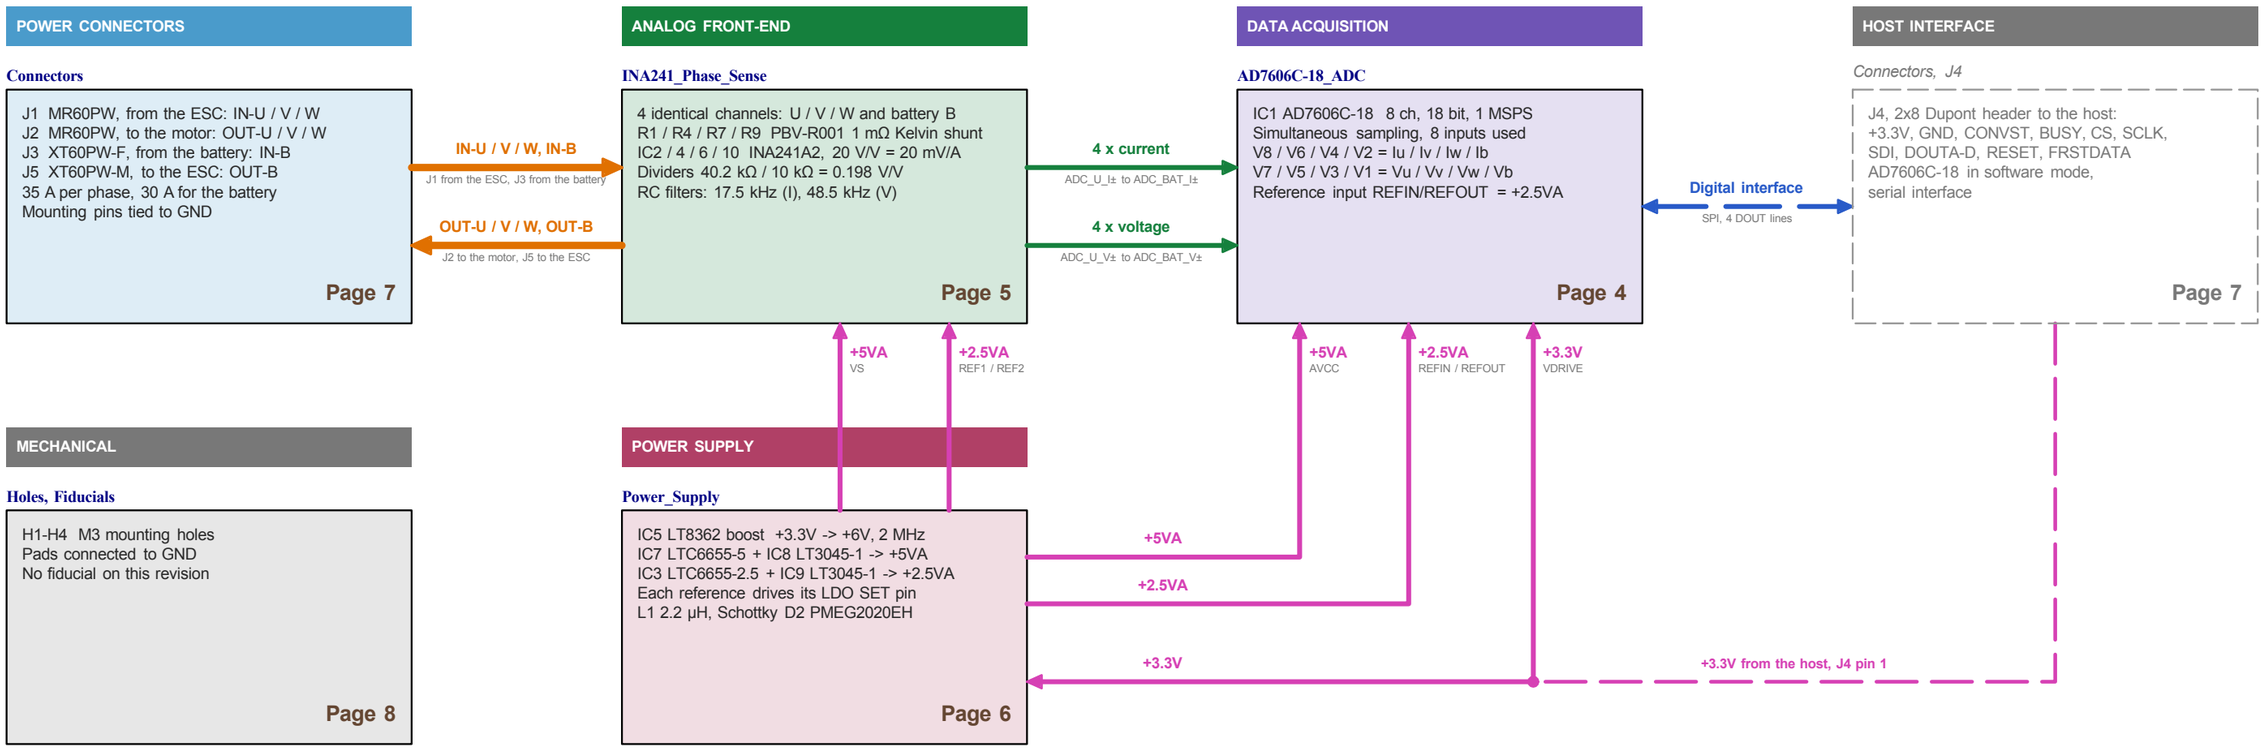


## LEGEND

- Power conductor: phases 35 A, battery 30 A
- Power rail
- Analog signal, differential pairs
- Digital interface (J4)
- Supply input from the host (J4)

## DOCUMENT INDEX


[1] Title Page
[2] Block Diagram
[3] Project Architecture
[4] AD7606C-18 ADC
[5] INA241 Phase Sensing
[6] Power Supply - Analog Rails
[7] Connectors
[8] Holes, Fiducials
[9] Power Sequencing
[10] Revision History


| | | | | |
|---|---|---|---|---|
| Comments: | Company: OPEN THRUST LAB | | Variant: | Git Hash: 04dd92c |
| | Board Name: PHASETRACKER | | Project Name: OPEN_PHASE | |
| Sheet Title: Project Architecture | File Name: Project Architecture.kicad_sch | Designer: SIEBERT DIMITRY | Date: 2026-10-11 | Revision: + (Unreleased) |
| Sheet Path: /Project Architecture/ | | Reviewer: | Size: A3 | Sheet: 3 of 10 |