
[3] Project Architecture

Sheet hierarchy and signal flow. Click a block or its page number to open the sheet.

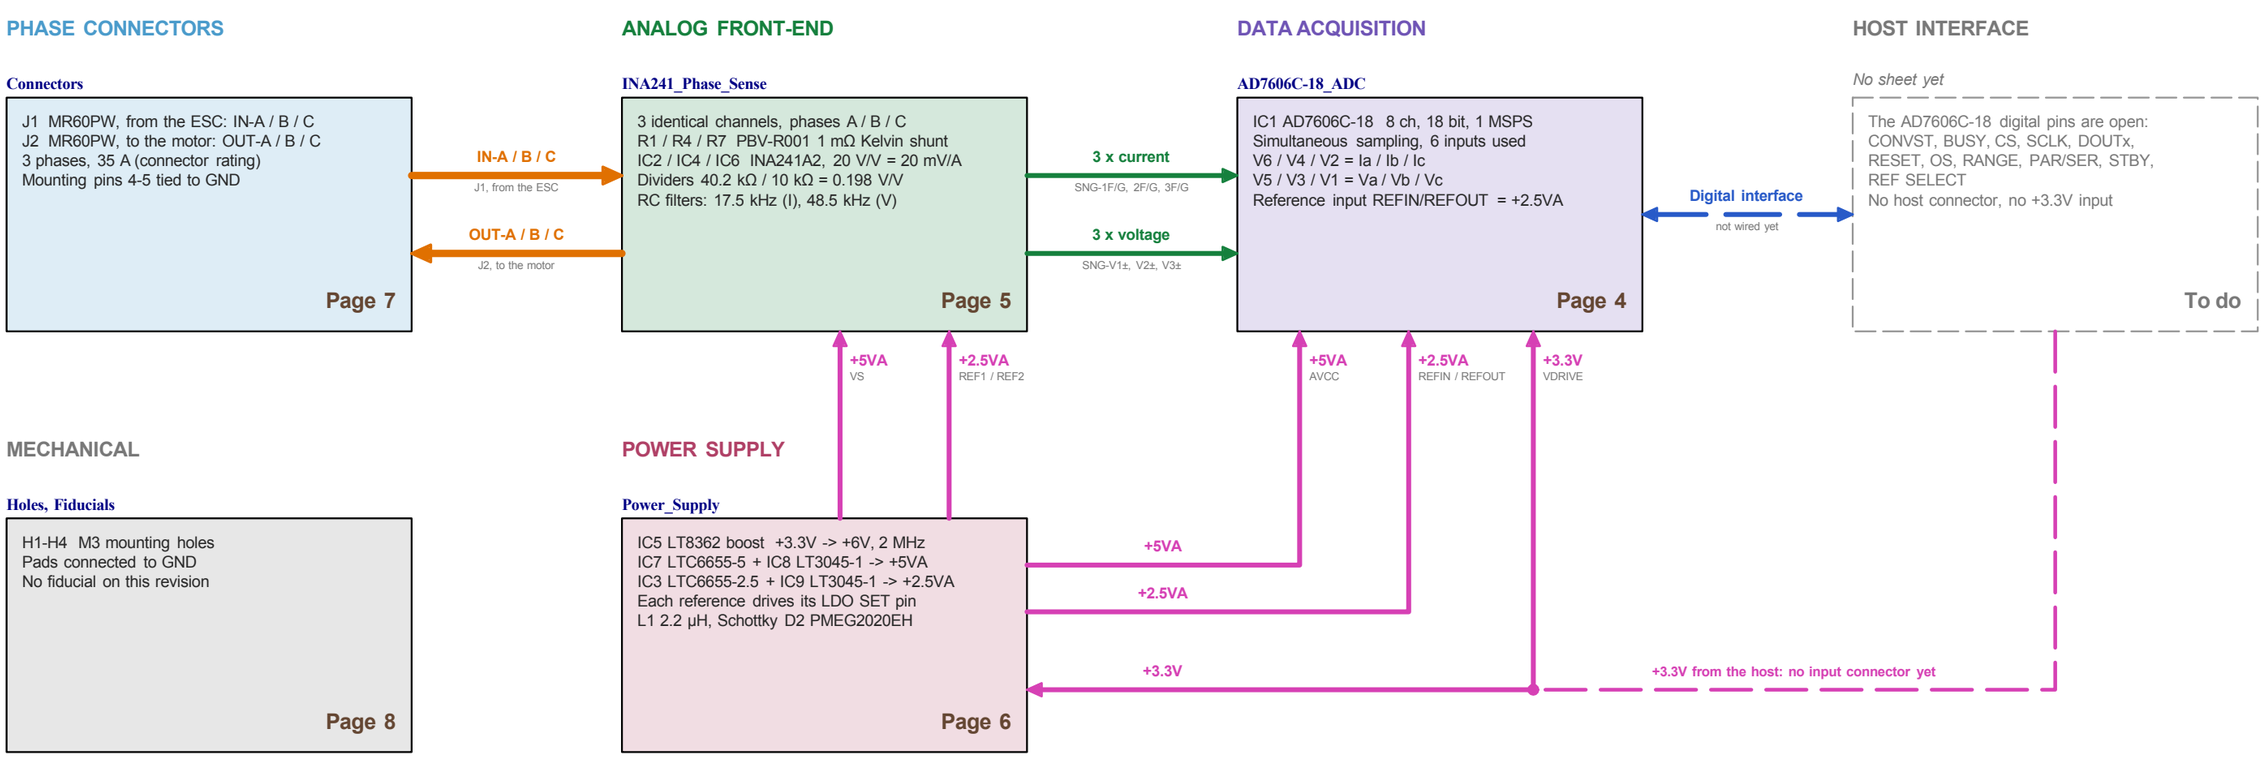

LEGEND

- Phase conductor, 35 A
- Power rail
- Analog signal, differential pairs
- Digital interface, not wired yet
- Supply input, no connector yet

DOCUMENT INDEX

[1] Title Page
[2] Block Diagram
[3] Project Architecture
[4] AD7606C-18 ADC
[5] INA241 Phase Sensing
[6] Power Supply - Analog Rails
[7] Connectors
[8] Holes, Fiducials
[9] Power Sequencing
[10] Revision History

Comments:	Company: OPEN THRUST LAB		Variant:	Git Hash: 7703dc5
	Board Name: PHASETRACKER		Project Name: OPEN_PHASE	
Sheet Title: Project Architecture	File Name: Project Architecture.kicad_sch	Designer: SIEBERT DIMITRY	Date: 2026-10-06	Revision: + (Unreleased)
Sheet Path: /Project Architecture/		Reviewer:	Size: A3	Sheet: 3 of 10